


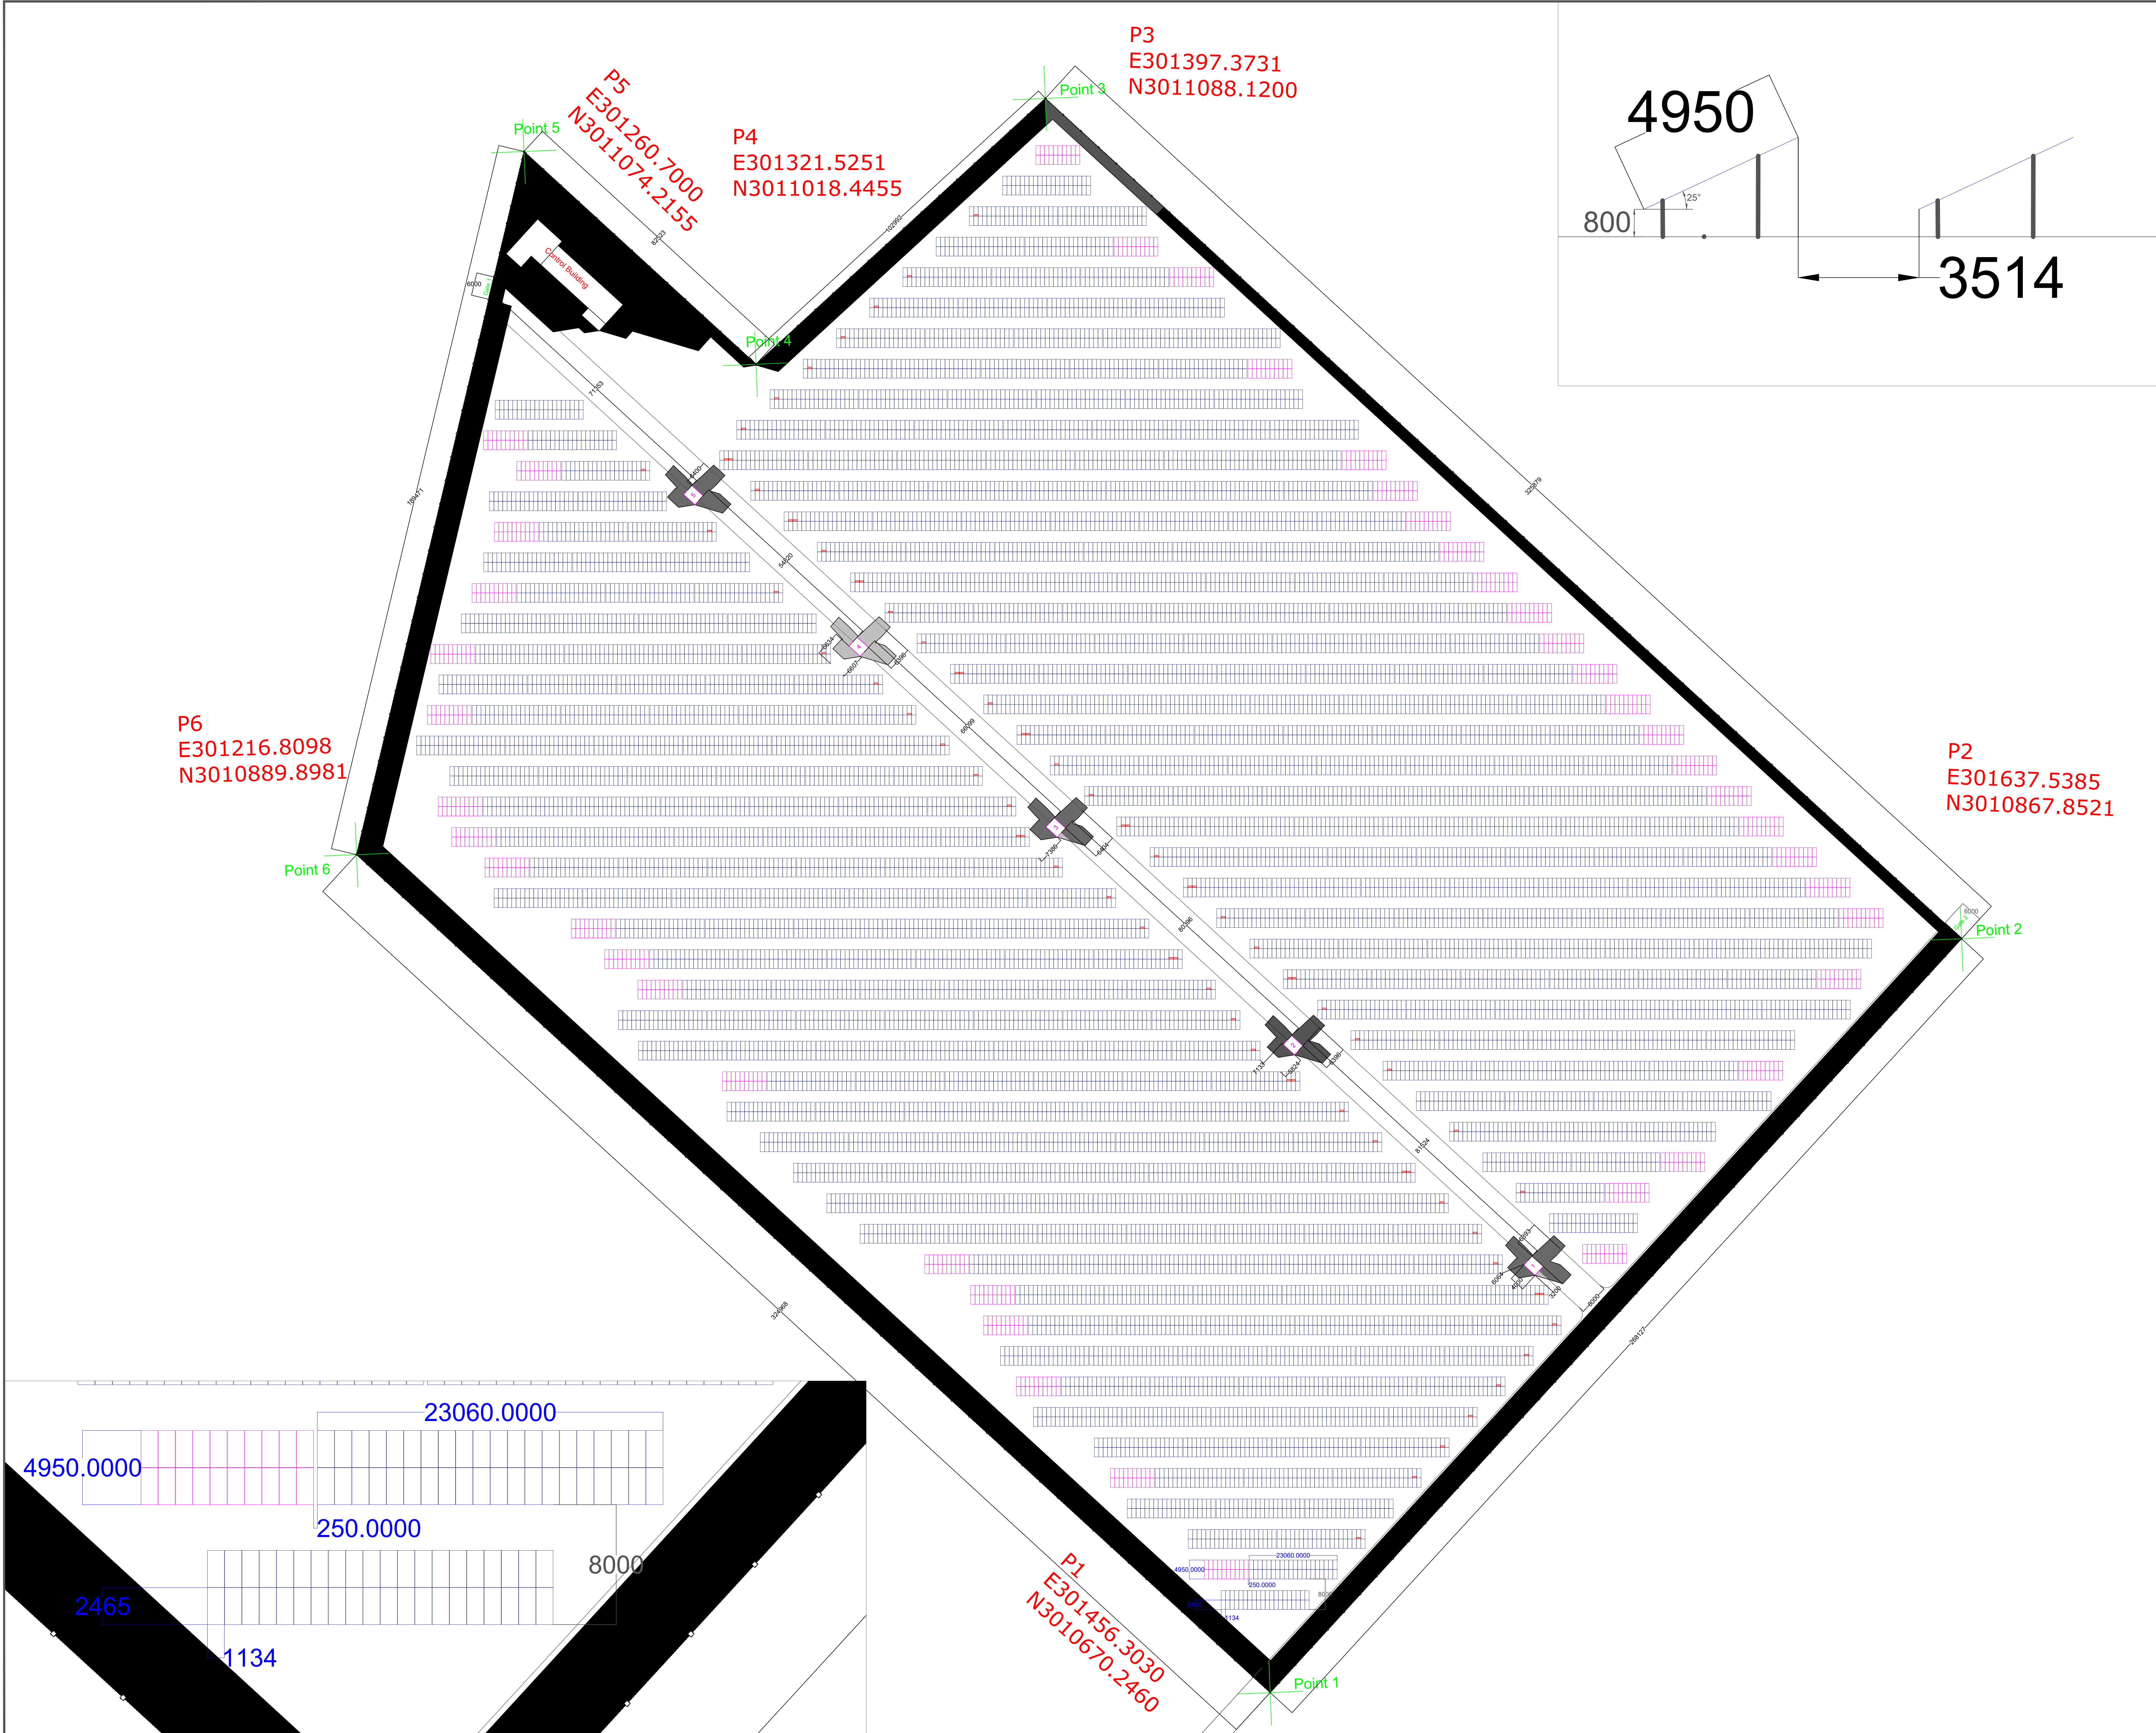

Legend:

PV Module Table (2x20)

PV Module Table (2x10)

String Inverter

Fence

Shadow @ (21/12 & 21/7)

Transformer

Site Info

Orientation	Location		
	Country	Egypt	
	City	Asyut	
	Coordinates		
	Point	Northing	Easting
	1	3010670.246	301456.303
	2	3010867.8521	301637.539
3	3011088.120	301397.373	
4	3011018.446	301321.525	
5	3011074.216	301260.700	
6	3010889.898	301216.810	

General Notes:

- All dimensions are in millimeters, unless otherwise indicated.
- All modules' lowest elevation is 800 mm.

System Specifications

No. of Modules	15,880
No. of Strings	794
No. of modules per string	20
Module Wp	630
No. of Inverters	75
Inverter Nominal Power	115 kVA
Transformer	5x2,000 kVA
DC Capacity @ STC	10,004.4 kWp
AC Capacity @ 30°C	8,625 kW AC
Substructure	Fixed
Tilt	25°
Pitch	8 m
DC/AC	1.16
String	1,049.4 Vdc
Grid Voltage	6.6 kVac

Drawing Notes:

- Fence Height is 2.5m.

No.	Description	By	Check	Approved	Date
04	Issued for Approval	AM	RS	AH	7/9/25
03	Issued for Approval	AM	RS	AH	27/8/25
02	Issued for Approval	AM	RS	AH	23/6/25
01	Issued for Approval	AM	RS	AH	01/6/25
00	Issued for comments	YT	RS	RS	17/2/25

Status: Design Drawing

EPC Contractor:

Infinity E. Egypt
57 Nile Kornish St., 7th Floor
Mokki, Cairo, Egypt, 11431
Tel: +202 25 228 860
Fax: +202 25 28 2268
Mail: info@weareinfinity.com
Web: www.weareinfinity.com

Project: ASORC, 10MWp Green Electrical Power Generation Plant From PV Solar Energy—On Grid

Client: ASORC—Asyut Petroleum Refinery

Drawing Name: PV Layout

Scale (A0)	Drawing No.	Rev.
1:530	2358-ASORC-MECH-001	04